

COMUNE DI COLLESALVETTI - AOOCCOL - 01 - 0019693 - Ingresso - 17/09/2026 - 11:42


PARTICOLARE TECNICA NO-DIG
Scala 1:10

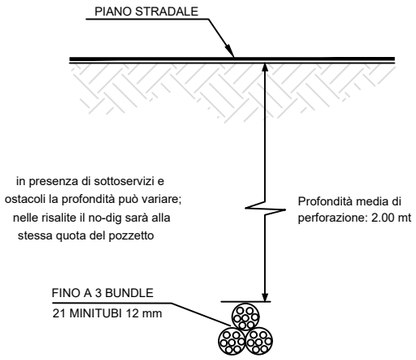


SEZIONE TIPO SCAVO TRADIZIONALE IN ASFALTO
Scala 1:10

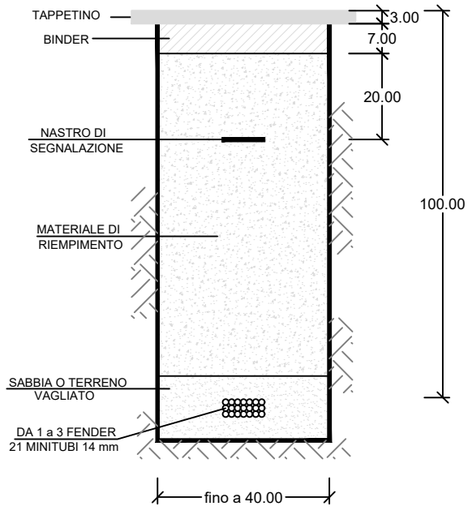


SEZIONE TIPO SCAVO TRADIZIONALE IN STERRATO
Scala 1:10

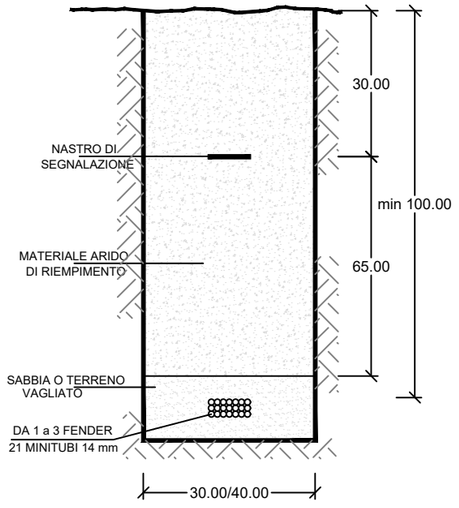


SCAVO A SEZIONE OBBLIGATA CON RIEMPIMENTO IN CEMENTO
Scala 1:10

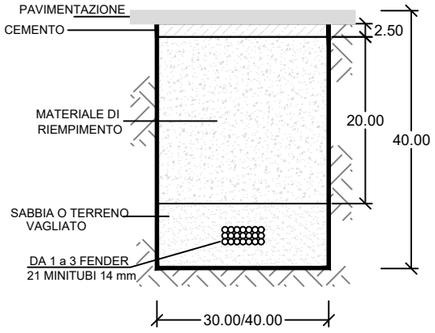

SEZIONE LONGITUDINALE TECNOLOGIA "NO DIG"

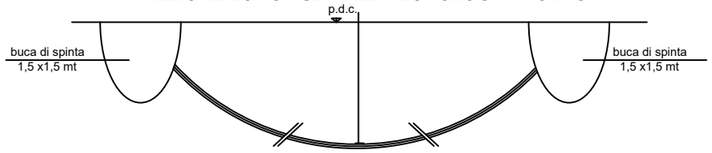


SEZIONE TIPO SCAVO IN ASFALTO IN MINITRINCEA TRADIZIONALE
Scala 1:10

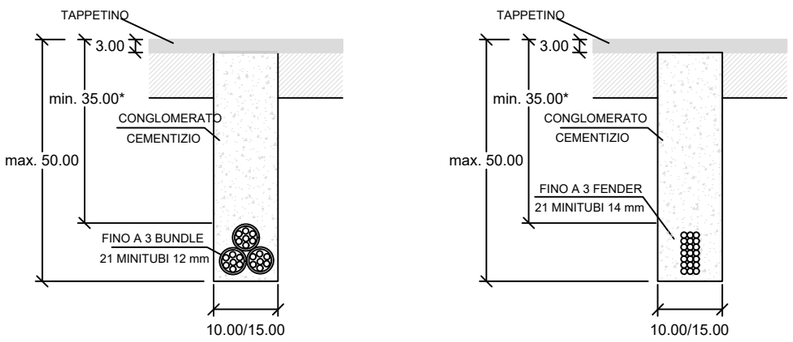


*La quota altimetrica del ricoprimento della struttura di contenimento dell'infrastruttura digitale è pari a:
- min. 40 cm in ambito extraurbano
- min. 35 cm in ambito urbano

PARTICOLARE TECNICA MICROTRINCEA
Scala 1:10

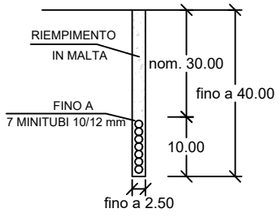

SEZIONE TIPO IN CANALA VTR/FeZn 175x70 mm
Scala 1:2

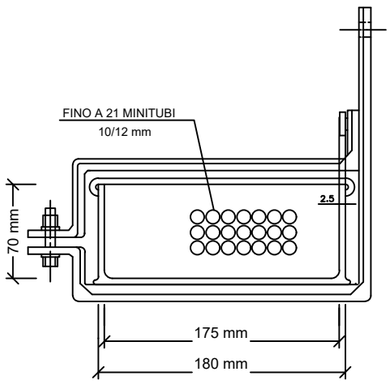

Particolari Costruttivi Scavi

Data: Gennaio 2026

Scala: Varie